



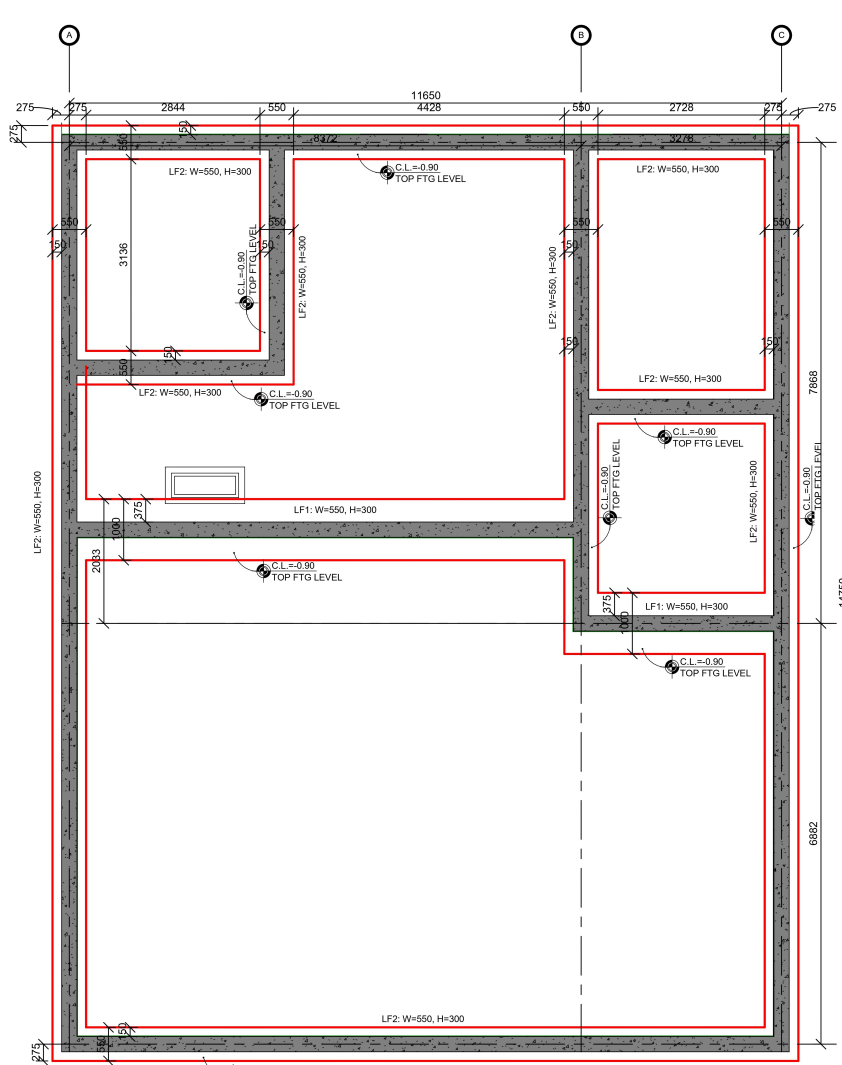


FOUNDATION FRAMING LAYOUT

1 : 50

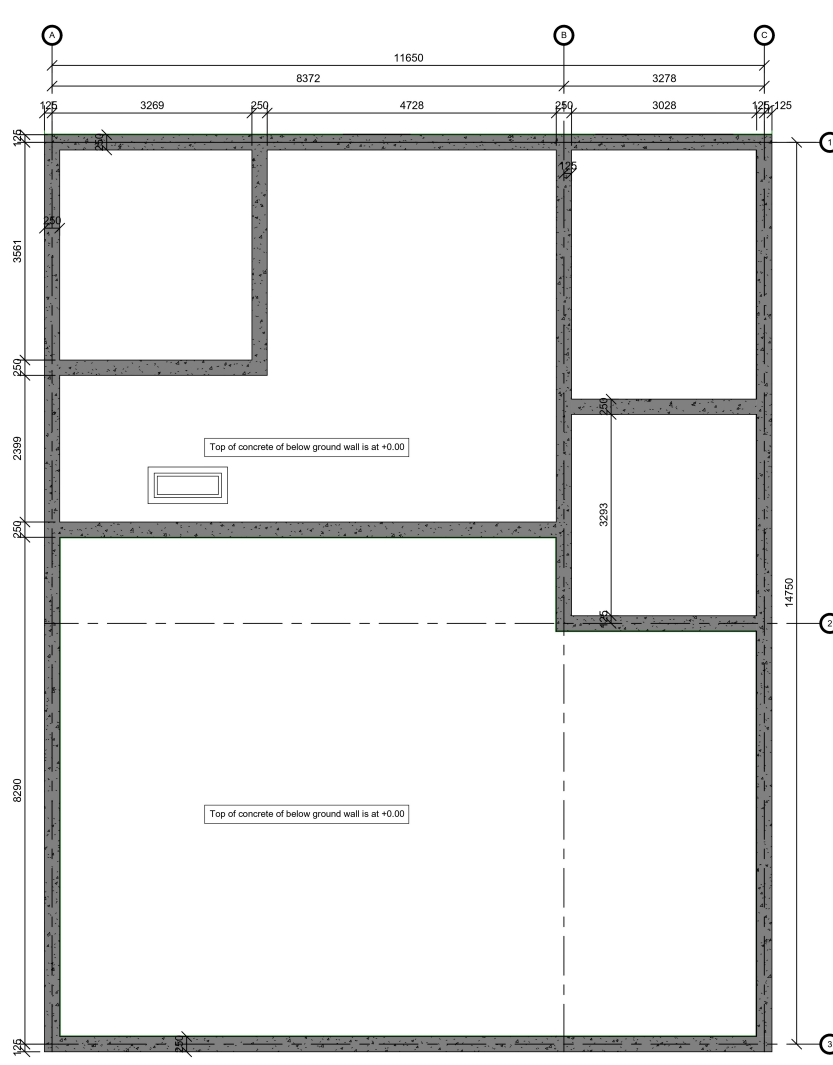


RC WALL BELOW GF FRAMING LAYOUT


1 : 50

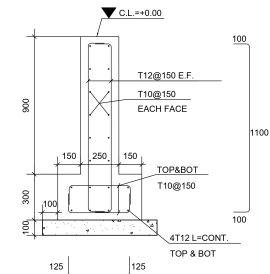


TYPICAL SECTION ON LF2
Sc.:1/25

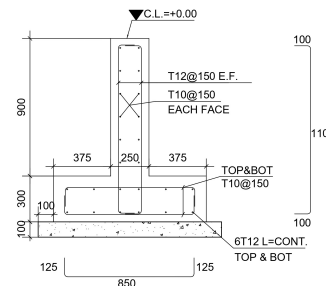


TYPICAL SECTION ON LF1
Sc.:1/25

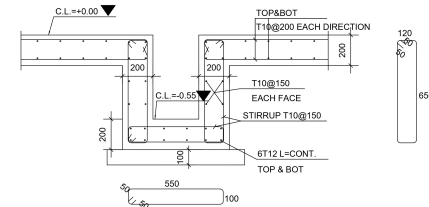

TYPICAL SECTION ON TRENCH AND SOG (Th=200) REINF DETAIL
Sc.:1/25

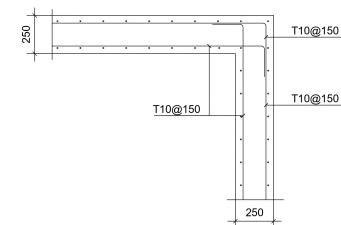

UNDERGROUND WALL CONNECTION -
HZ REINF DISTRIBUTION AT CORNERS
Sc.:1/25

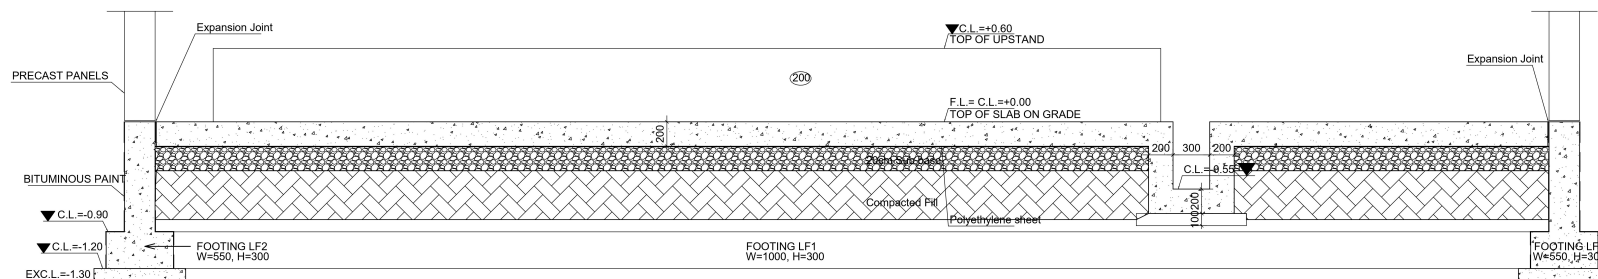

SECTION A-A

1 : 25

Makkah

