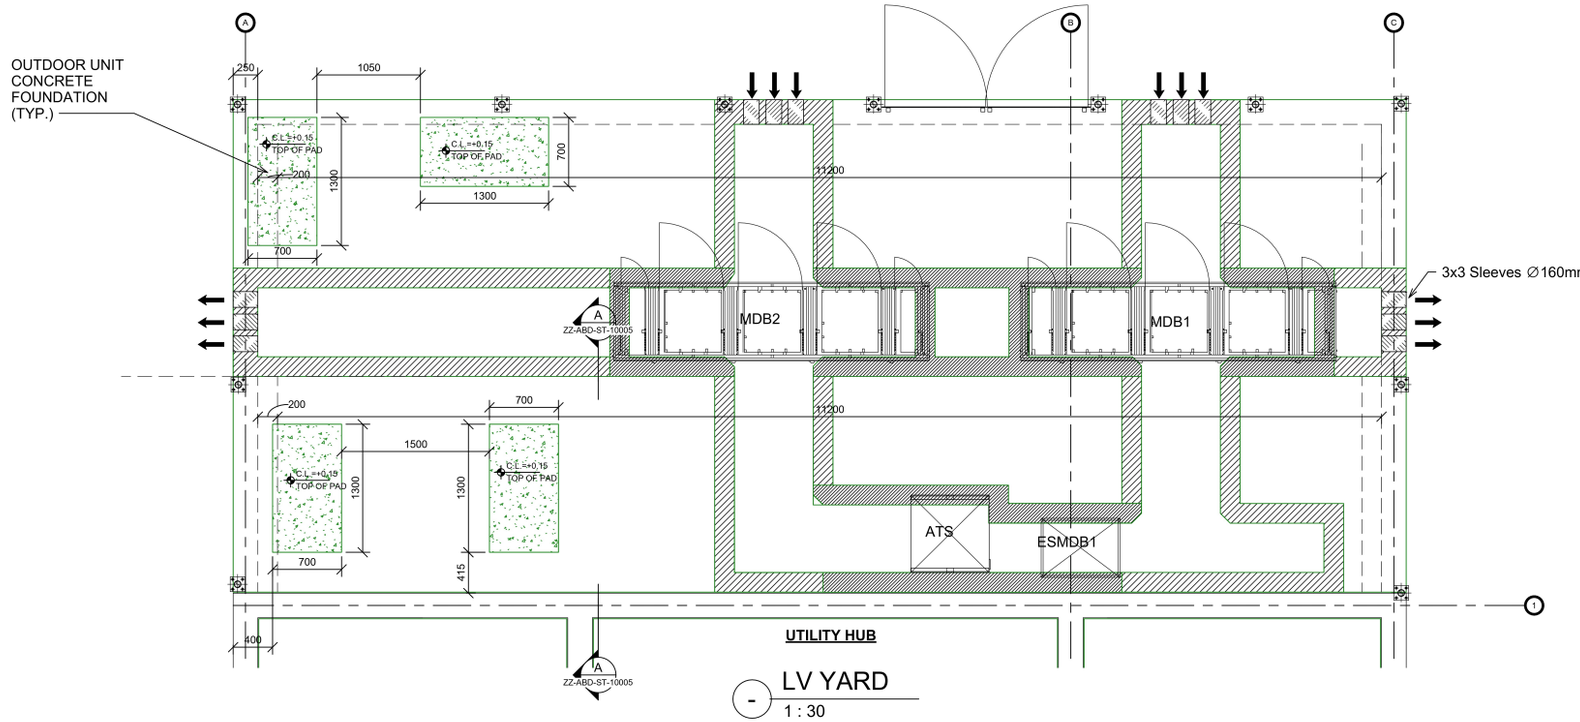

LV YARD

1 : 30

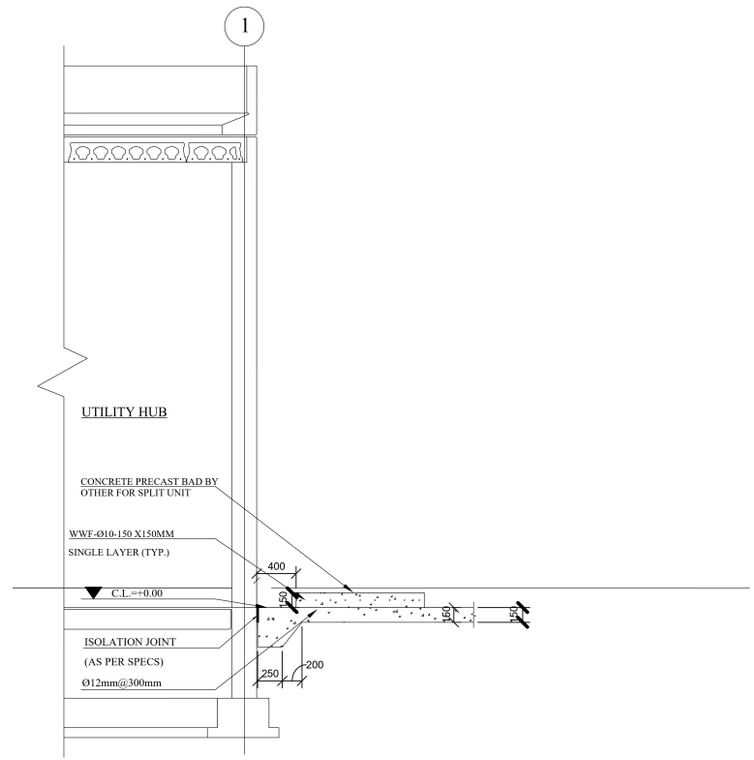

TYPICAL DETAILS FOR SPLIT UNIT FOUNDATION

SECTION A-A

ZZ-ABD-ST-10005 1 : 30